


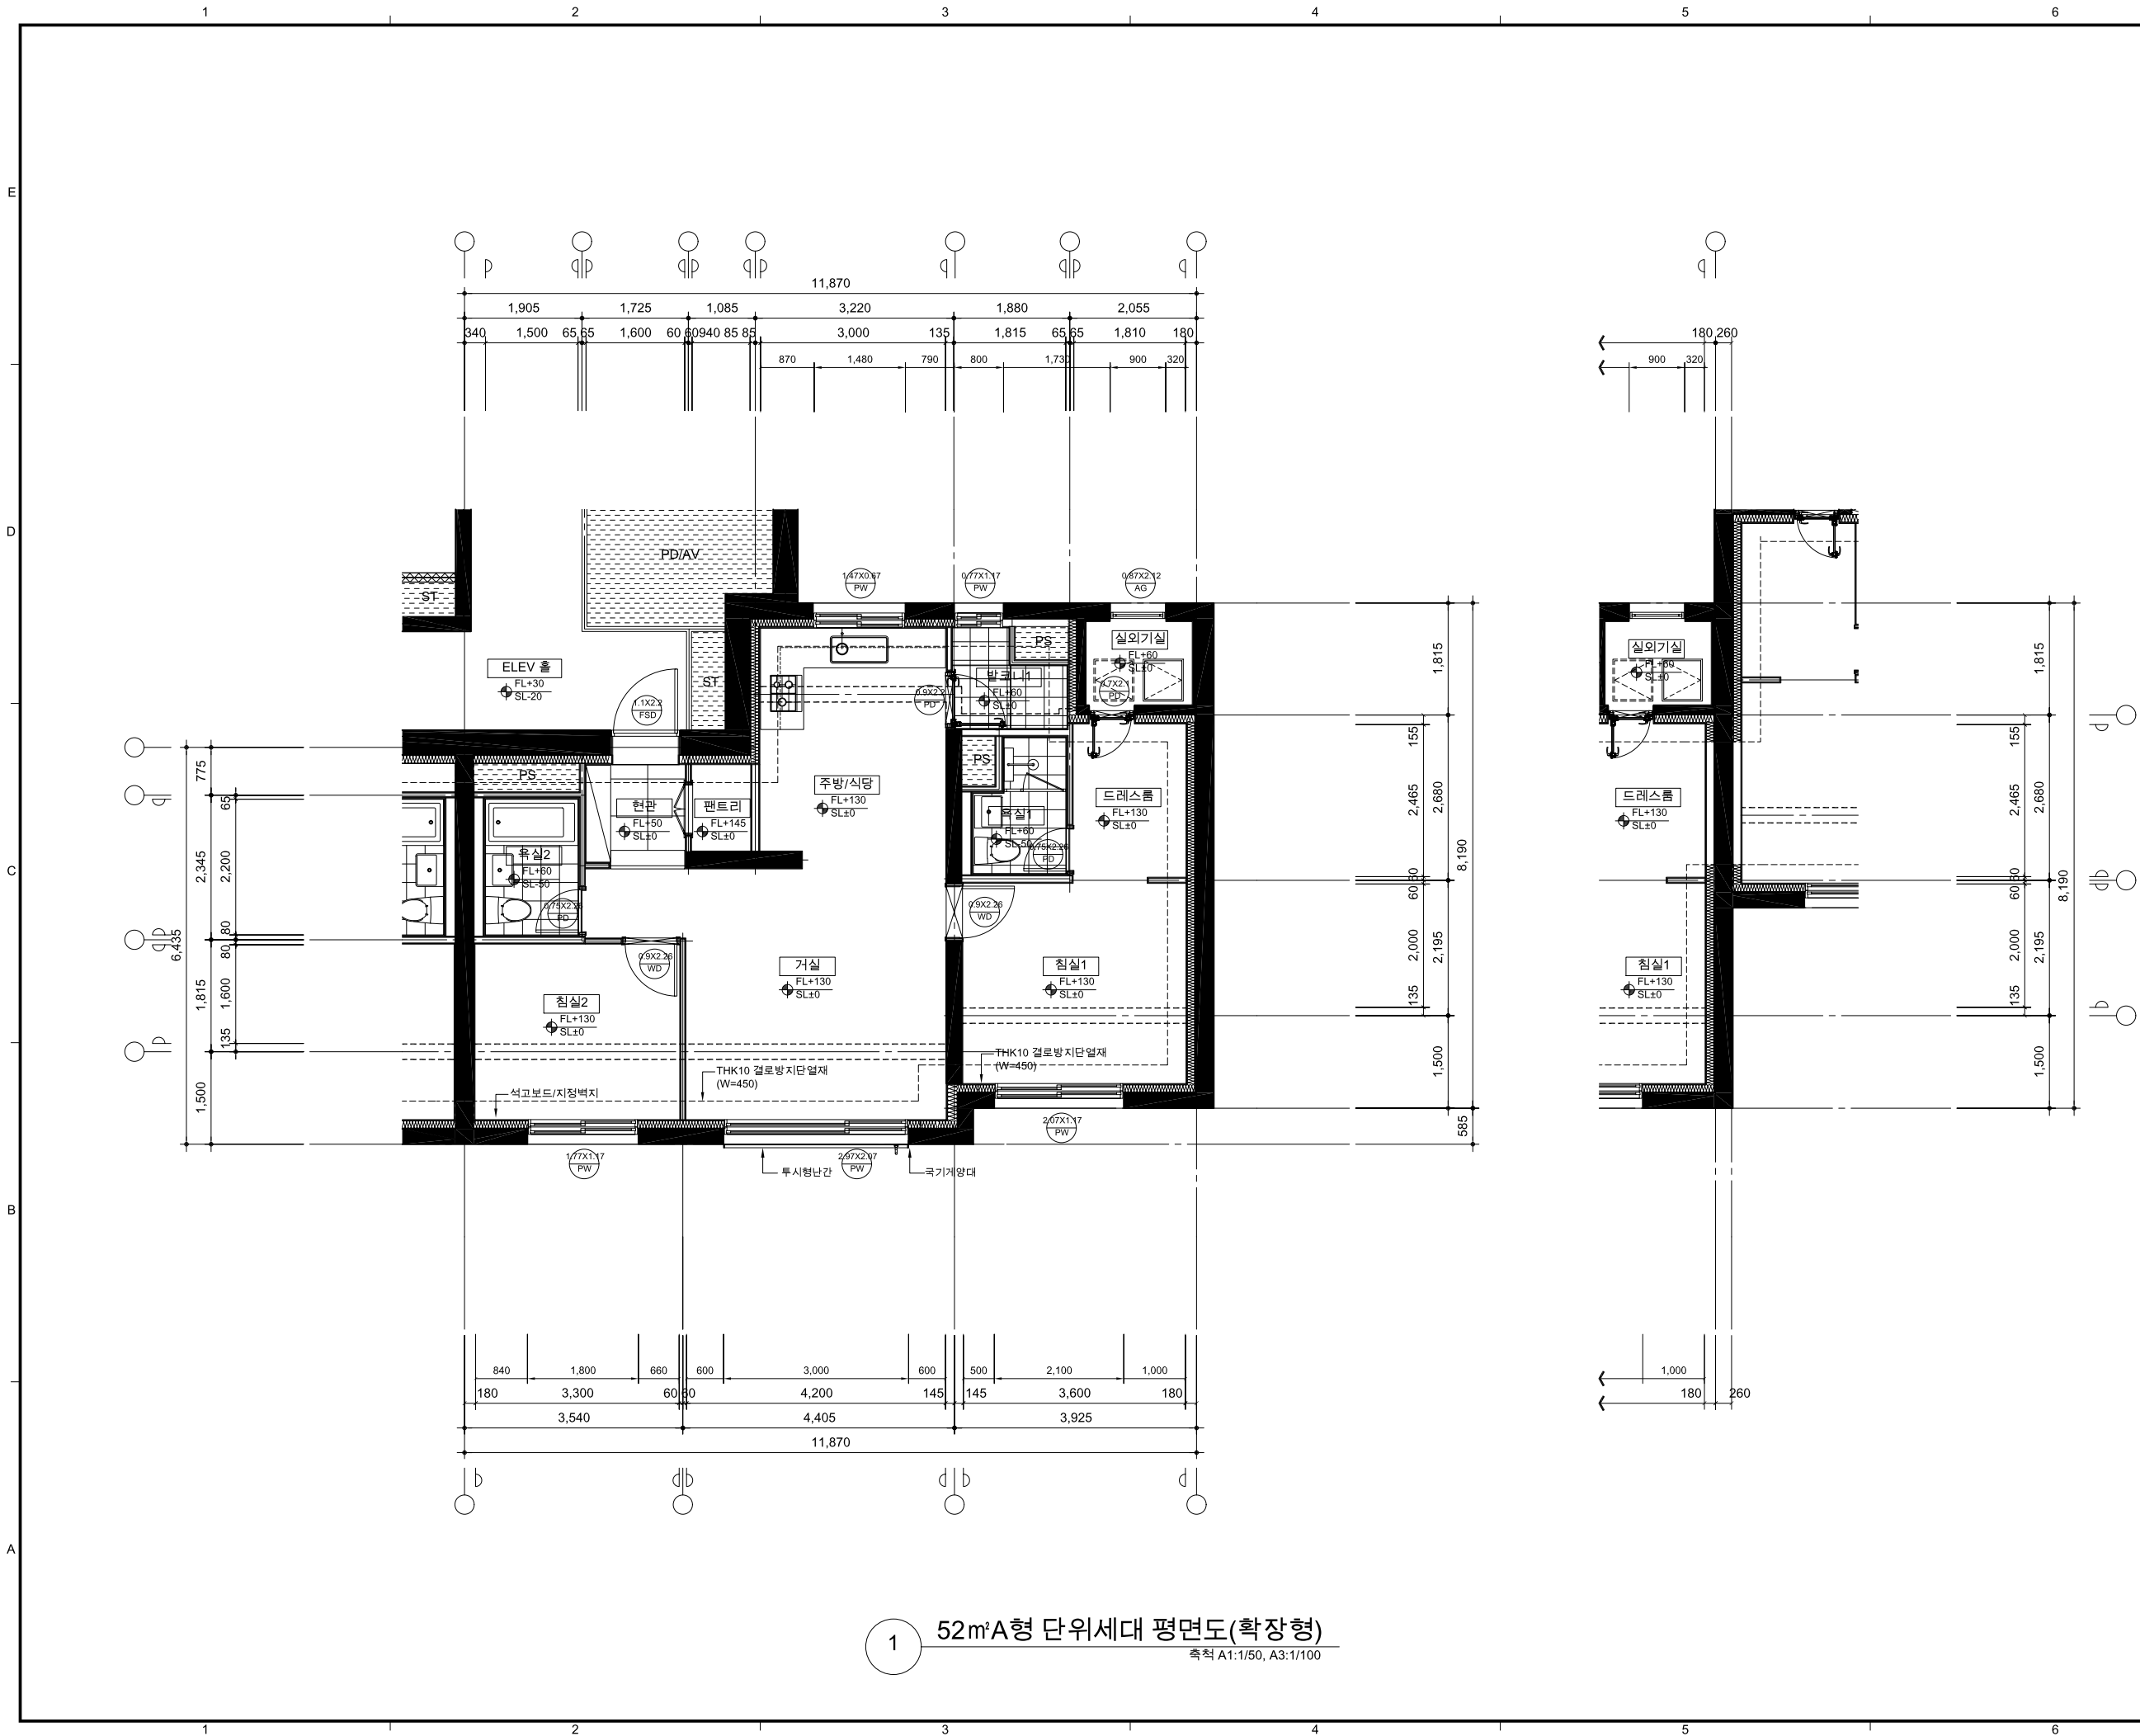


1 52m²A형 단위세대 평면도(확장형)
축척 A1:1/50, A3:1/100



- NOTE
1. 마감 및 재료의 적용기준이 도면간 상이할 경우 기본주택, 인테리어도면, 건축도면 순으로 적용하며 관계전문가와 협의하여 공사감독자의 확인 후 시공할 것.
 2. 부위별 마감은 실내마감재료를 참조하며, 각 세대의 마감은 기본주택 및 세대별 계약조건에 따라 변경될 수 있음.
 3. 천장평면도 및 욕실 확대평면도, 내부 도어 가구 등은 인테리어 도면을 참조할 것.
 4. 세대분전반, 통신단자함 등은 인테리어도면 및 전기/통신도면을 참조할 것.
 5. 『실내건축의 구조,시공방법등에 관한기준』에 적합한 마감 및 재료로 시공할 것.
 6. 설비 샤프트 내 층간 방화구획의 경계는 층간 슬래브이며, 슬래브를 관통하는 배관 주변은 「건축자재등 품질인정 및 관리기준」에 적합하게 채움할 것.
 7. 발코니 확장형세대와 기본형세대가 접하는 경우 기본형 세대 발코니 부위에 에너지 절약형 친환경주택의 건설기준에 적합한 단열조치를 할 것.
 8. 욕실, 발코니, 다용도실의 바닥 레벨은 평균 두께를 표현하였으며 시공 시 구배 등을 고려하여 편차가 발생될 수 있음.
 9. 바닥 배수드레인, 선출통, 수전의 개소와 위치는 실시공 시 변경될 수 있음.
 10. 세대 내 창호의 개폐방향은 실시공 시 변경될 수 있음.
 11. 세대 경계벽에는 공사용 통로가 설치될 수 있으며, 현장여건에 따라 위치 및 크기가 변경될 수 있음. (공사용 통로는 공사 후 차음, 내화구조 등 법적기준에 적합한 재료로 구축할 것.)
 12. 실외기실 내 하향식 피난구는 최하층 세대 (필로티 및 부대시설 상부세대 포함)의 바닥에는 설치되지 않음.

KEY PLAN

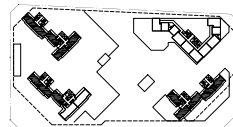

△			
	280	20	
△			
	280	20	
△			
	280	20	
수정번호	수정내용		
	작성일자	검토일자	승인일자

HAEAHN
ARCHITECTURE

(주)해안종합건축사사무소
서울특별시 강남구 봉은사로 208 해안빌딩 06135
T.3438 8000 F.3438 8100 www.haeahn.com

프로젝트명
화성동탄2 C-14BL
민간참여 공공주택 건설사업
도면명
52m²A형 단위세대 평면도
(확장형)

축
A1: 1/50 | A3: 1/100

PJ CODE	작성	검토	승인
23158	박창대	정독화	임형식
도면번호	20. 24. 08. 00.	20. 24. 08. 00.	20. 24. 08. 00.

A04-002